




VISTA FAÇANA CARRER

ESTUDIO DE LOCAL PARA LA  
SEDE DE LABORATORIO  
ECHEVARNE EN ANDORRA

CARRER PRAT DE LA CREU  
PARROQUIA D'ANDORRA LA VELLA  
ABRIL 2015

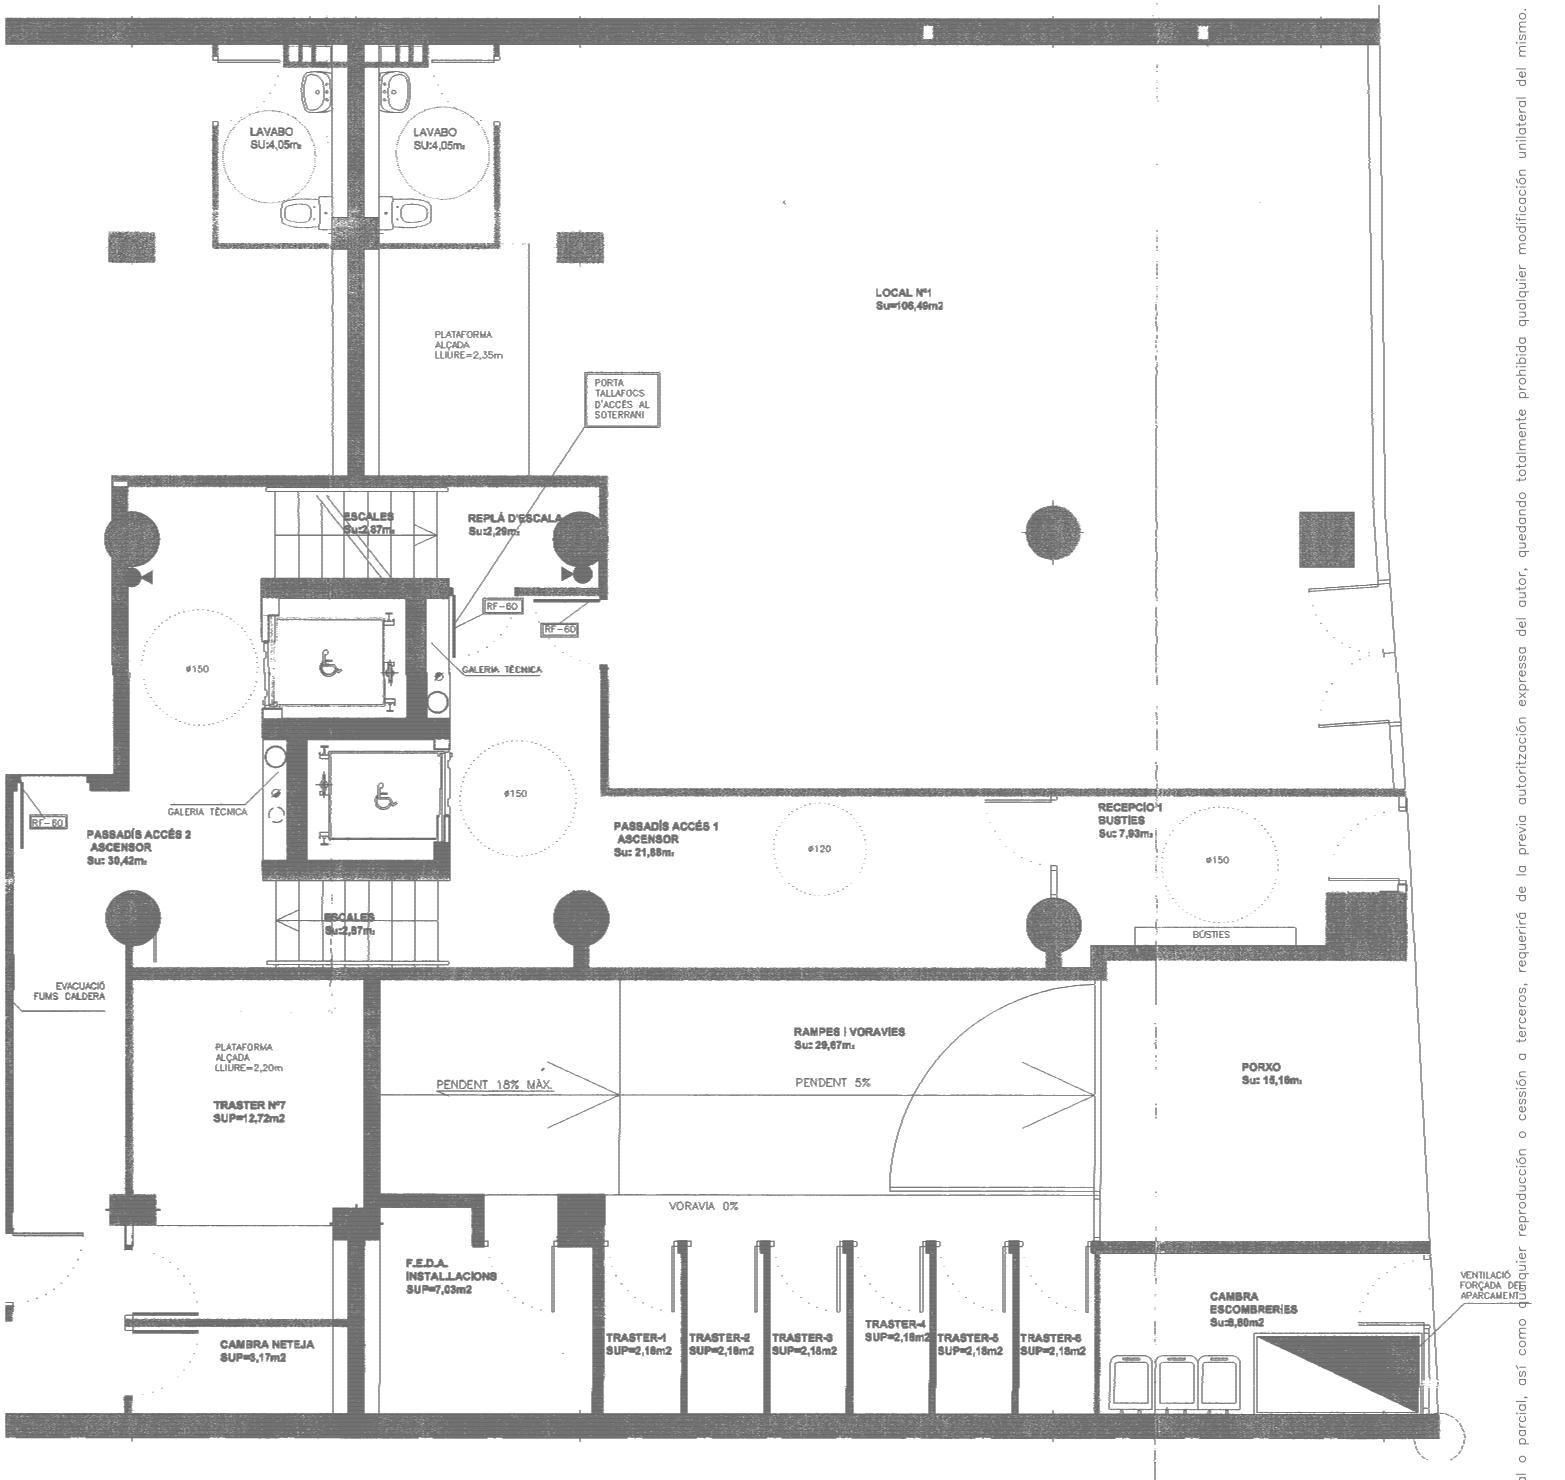

E01

ESTAT ACTUAL  
PLANTA BAIXA

1/100


ESTUDIO DE LOCAL PARA LA  
SEDE DE LABORATORIO  
ECHEVARNE EN ANDORRA

CARRER PRAT DE LA CREU  
PARROQUIA D'ANDORRA LA VELLA  
ABRIL 2015

PLANTA BAIXA  
SUPERFICIE CONSTRUIDA (\*) 121m<sup>2</sup>  
(\*) INCLUIDA BANCADA SOBRE RAMPA 6,2m<sup>2</sup>

lantia

lantia@lantia.com

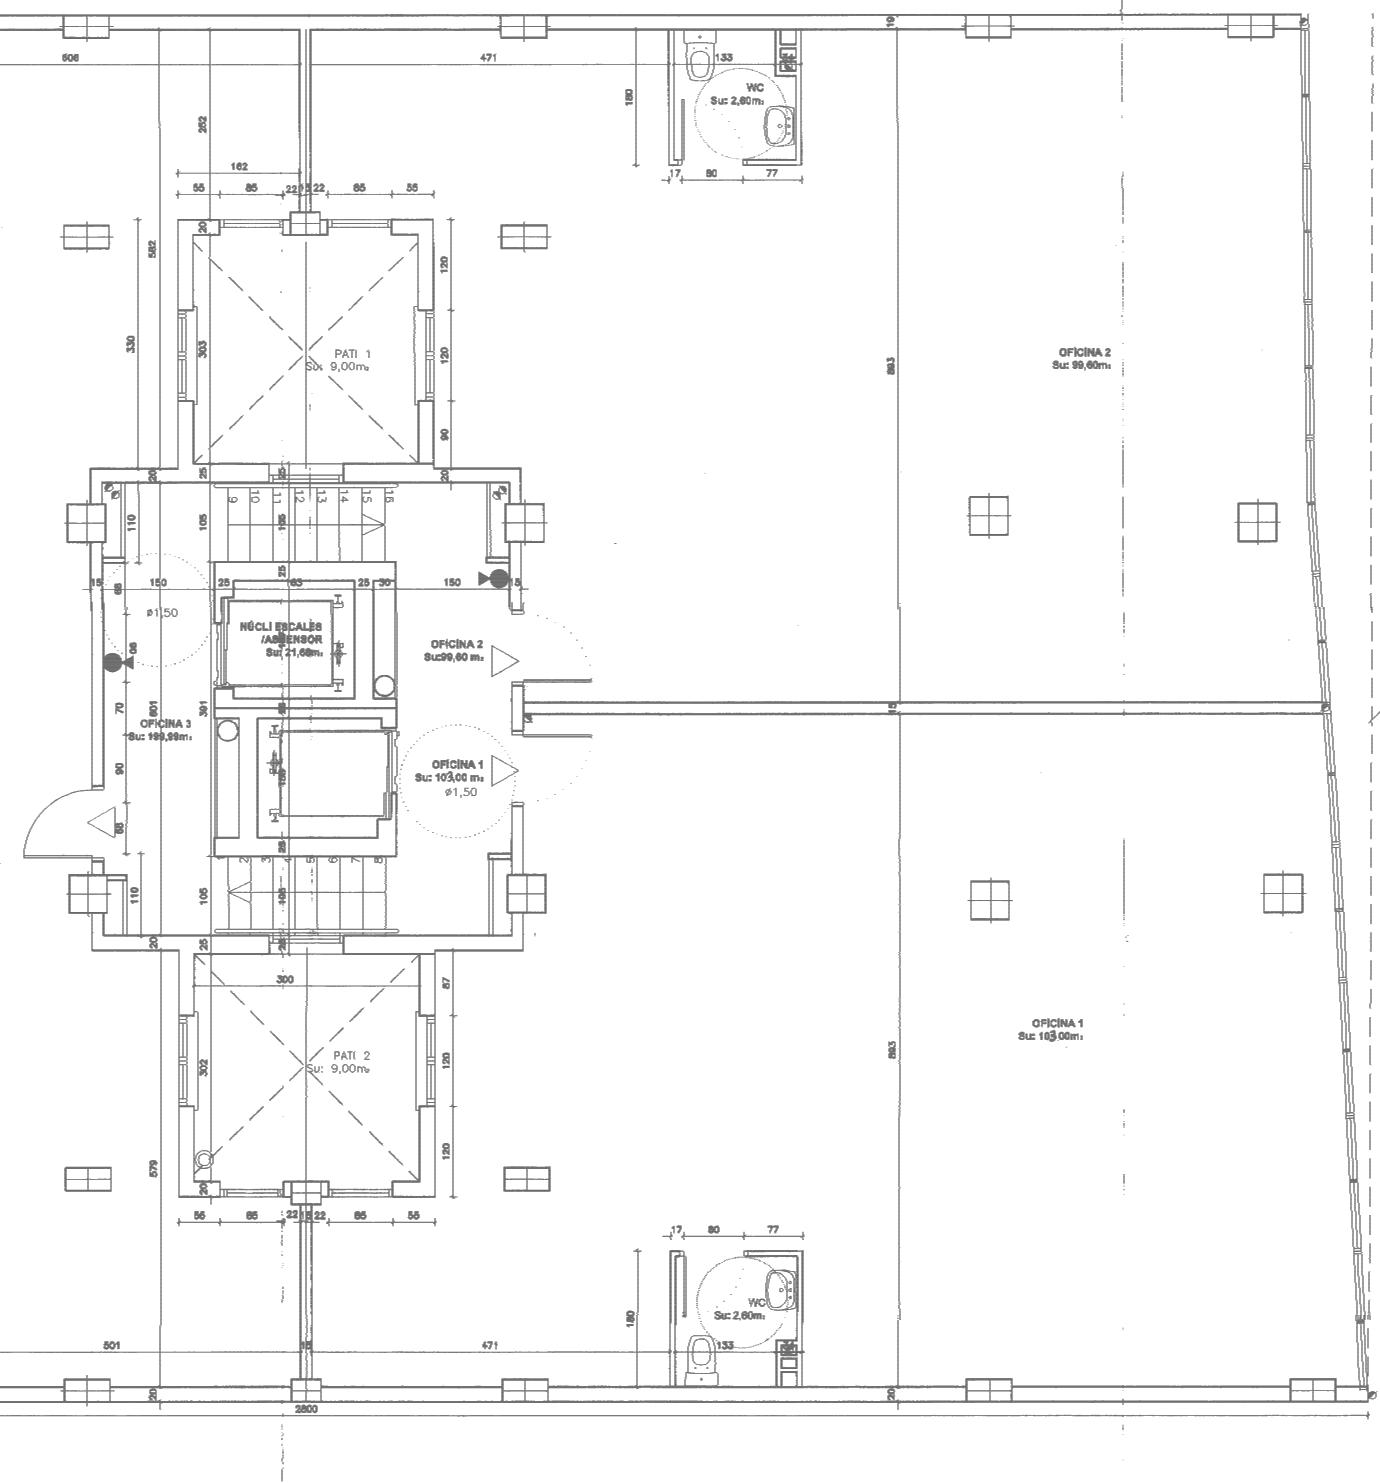

E02

ESTAT ACTUAL  
PLANTA PRIMERA

1/100

ESTUDIO DE LOCAL PARA LA  
SEDE DE LABORATORIO  
ECHEVARNE EN ANDORRA

CARRER PRAT DE LA CREU  
PARROQUIA D'ANDORRA LA VELLA  
ABRIL 2015

PLANTA PRIMERA  
SUPERFICIE CONSTRUIDA 105m<sup>2</sup>

lantia

lantia@lantia.com



### PLANTA PRIMERA

SUPERFICIE CONSTRUIDA	105m <sup>2</sup>
SUPERFICIE ÚTIL	96m <sup>2</sup>

### PLANTA BAIXA

SUPERFICIE CONSTRUIDA (*)	121m <sup>2</sup>
SUPERFICIE ÚTIL	107m <sup>2</sup>


(\*) INCLUIDA BANCADA SOBRE RAMPA 6,2m<sup>2</sup>

ESTUDIO DE LOCAL PARA LA SEDE DE LABORATORIO ECHEVARNE EN ANDORRA

CARRER PRAT DE LA CREU  
PARROQUIA D'ANDORRA LA VELLA  
ABRIL 2015

 lantia

lantia@lantia.com

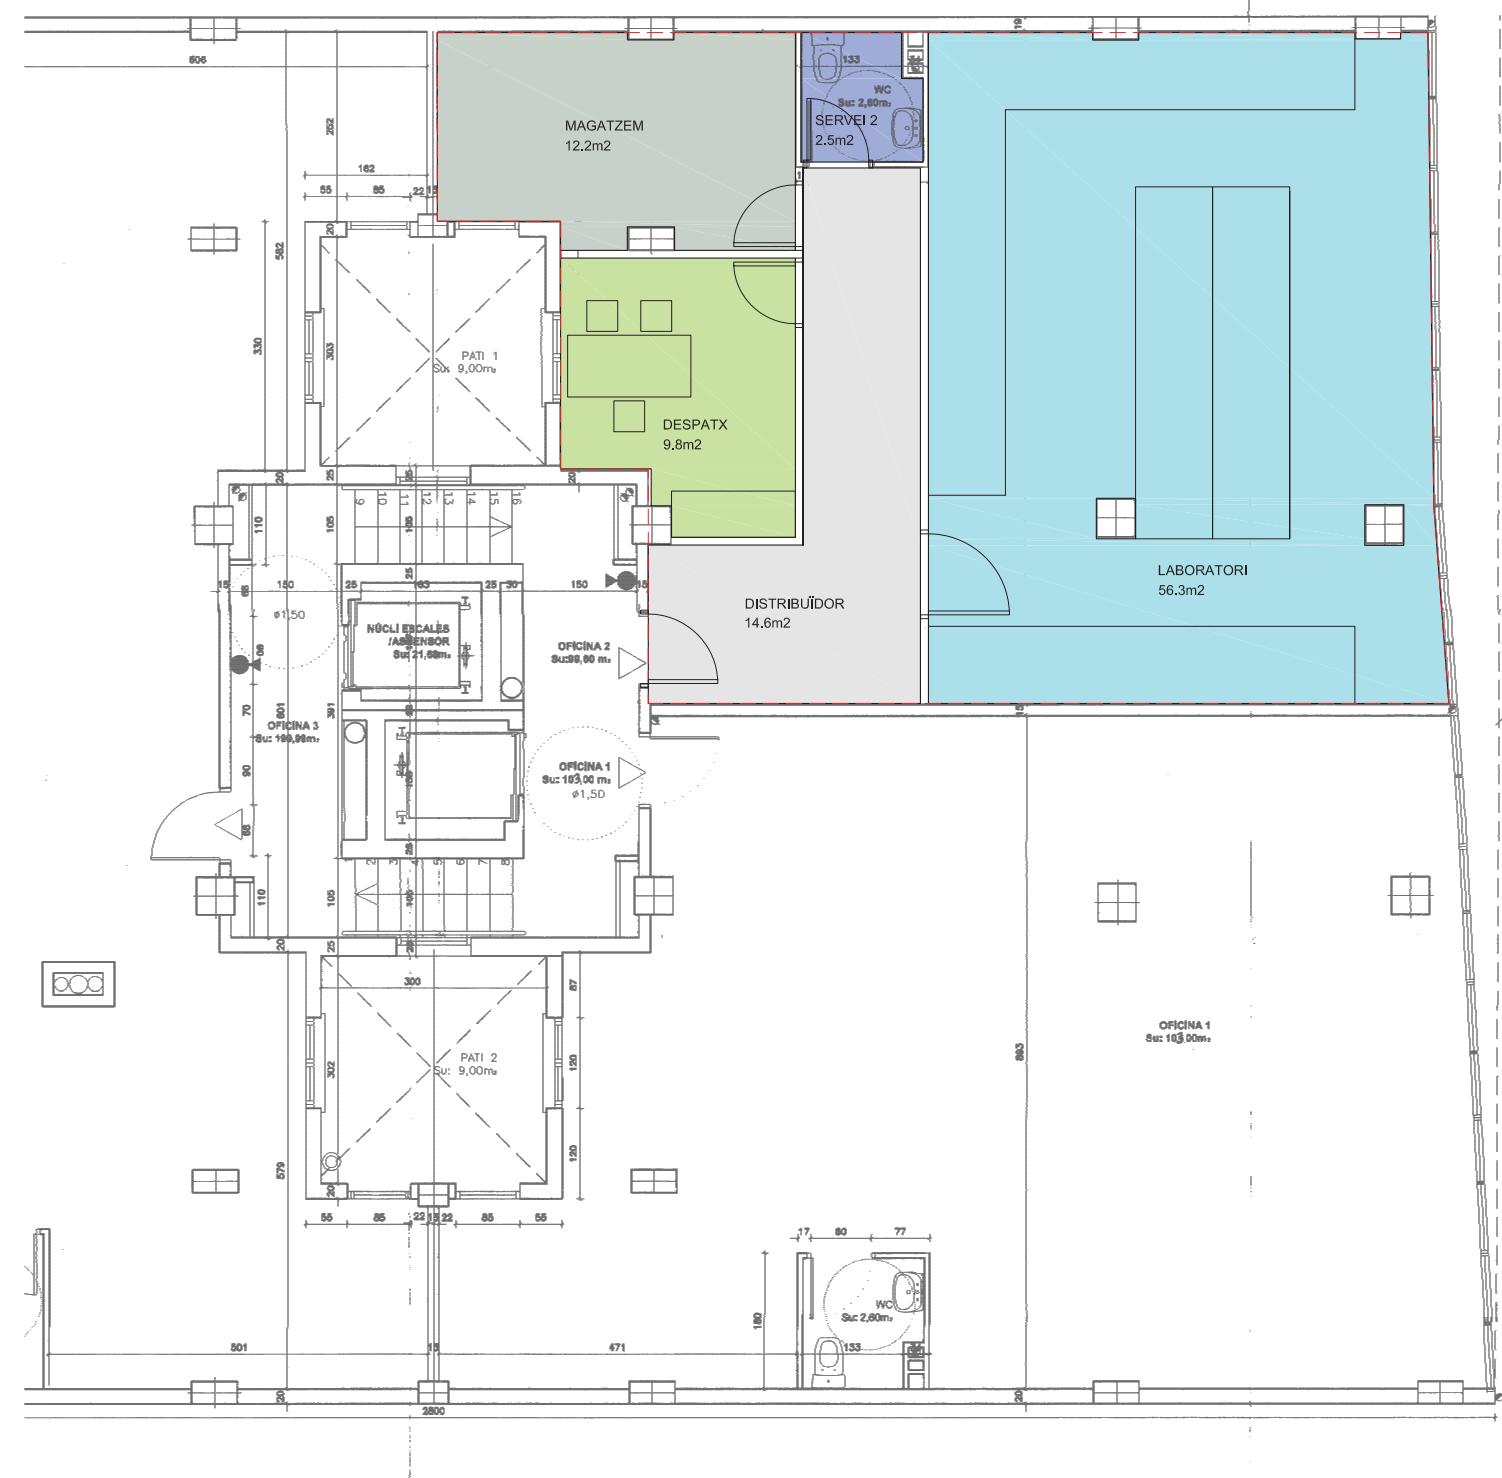

A 01

PROPOSTA A  
PLANTA PRIMERA

1/100

ESTUDIO DE LOCAL PARA LA  
SEDE DE LABORATORIO  
ECHEVARNE EN ANDORRA

CARRER PRAT DE LA CREU  
PARROQUIA D'ANDORRA LA VELLA  
ABRIL 2015

PLANTA PRIMERA

SUPERFICIE CONSTRUIDA	105m <sup>2</sup>
SUPERFICIE ÚTIL	96m <sup>2</sup>

PLANTA BAIXA

SUPERFICIE CONSTRUIDA (*)	121m <sup>2</sup>
SUPERFICIE ÚTIL	107m <sup>2</sup>

(\*) INCLUIDA BANCADA SOBRE RAMPA 6,2m<sup>2</sup>

lantia

lantia@lantia.com